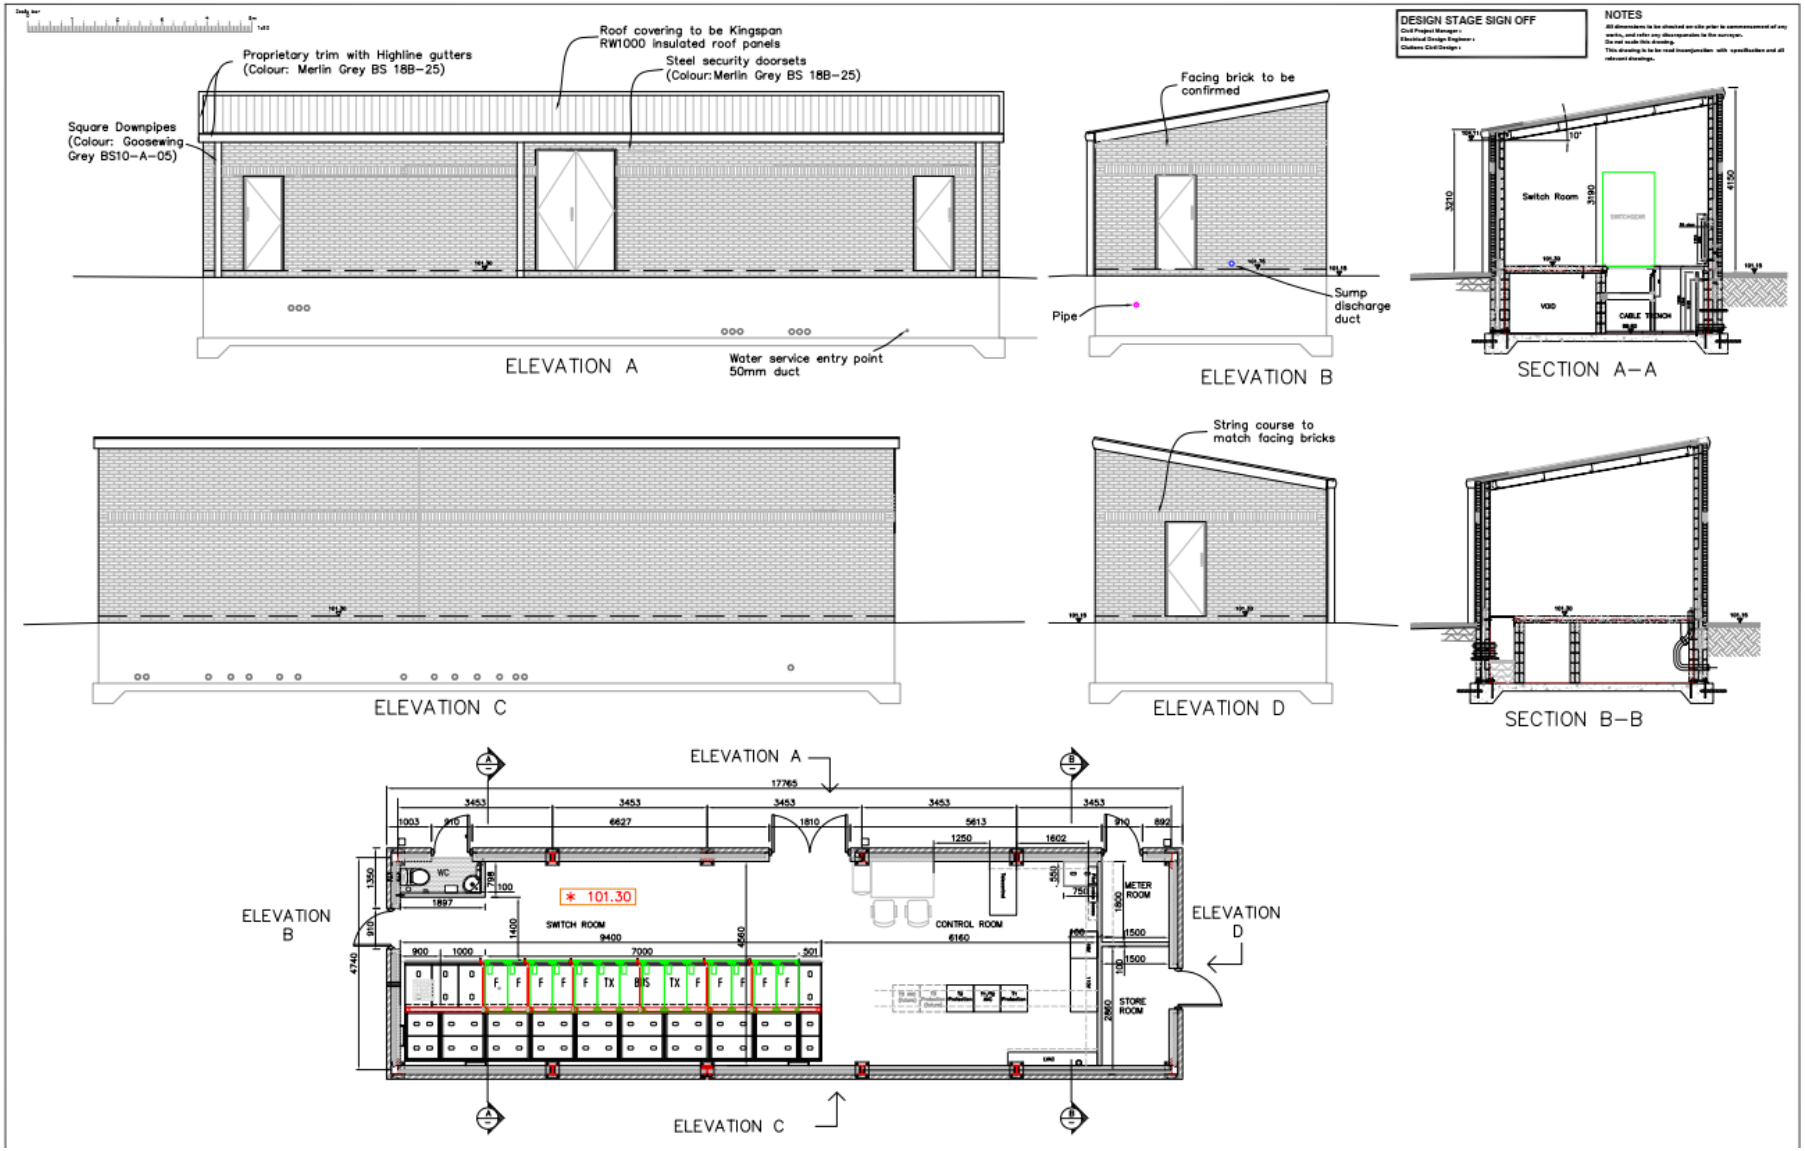

DESIGN STAGE SIGN OFF
NOTES
Proprietary trim with Highline gutters (Colour: Merlin Grey BS 18B-25)
Roof covering to be Kingspan RW1000 insulated roof panels
Steel security doorsets (Colour:Merlin Grey BS 18B-25)
Square Downpipes (Colour: Goosewing Grey BS10-A-05)
ELEVATION A
Water service entry point 50mm duct
Facing brick to be confirmed
Pipe
Sump discharge duct
ELEVATION B
Switch Room
VOID
CABLE TRENCH
SECTION A-A
ELEVATION C
String course to match facing bricks
ELEVATION D
SECTION B-B
ELEVATION A
ELEVATION B
ELEVATION D
ELEVATION C
WC
SWITCH ROOM
CONTROL ROOM
METER ROOM
STORE ROOM
* 101.30